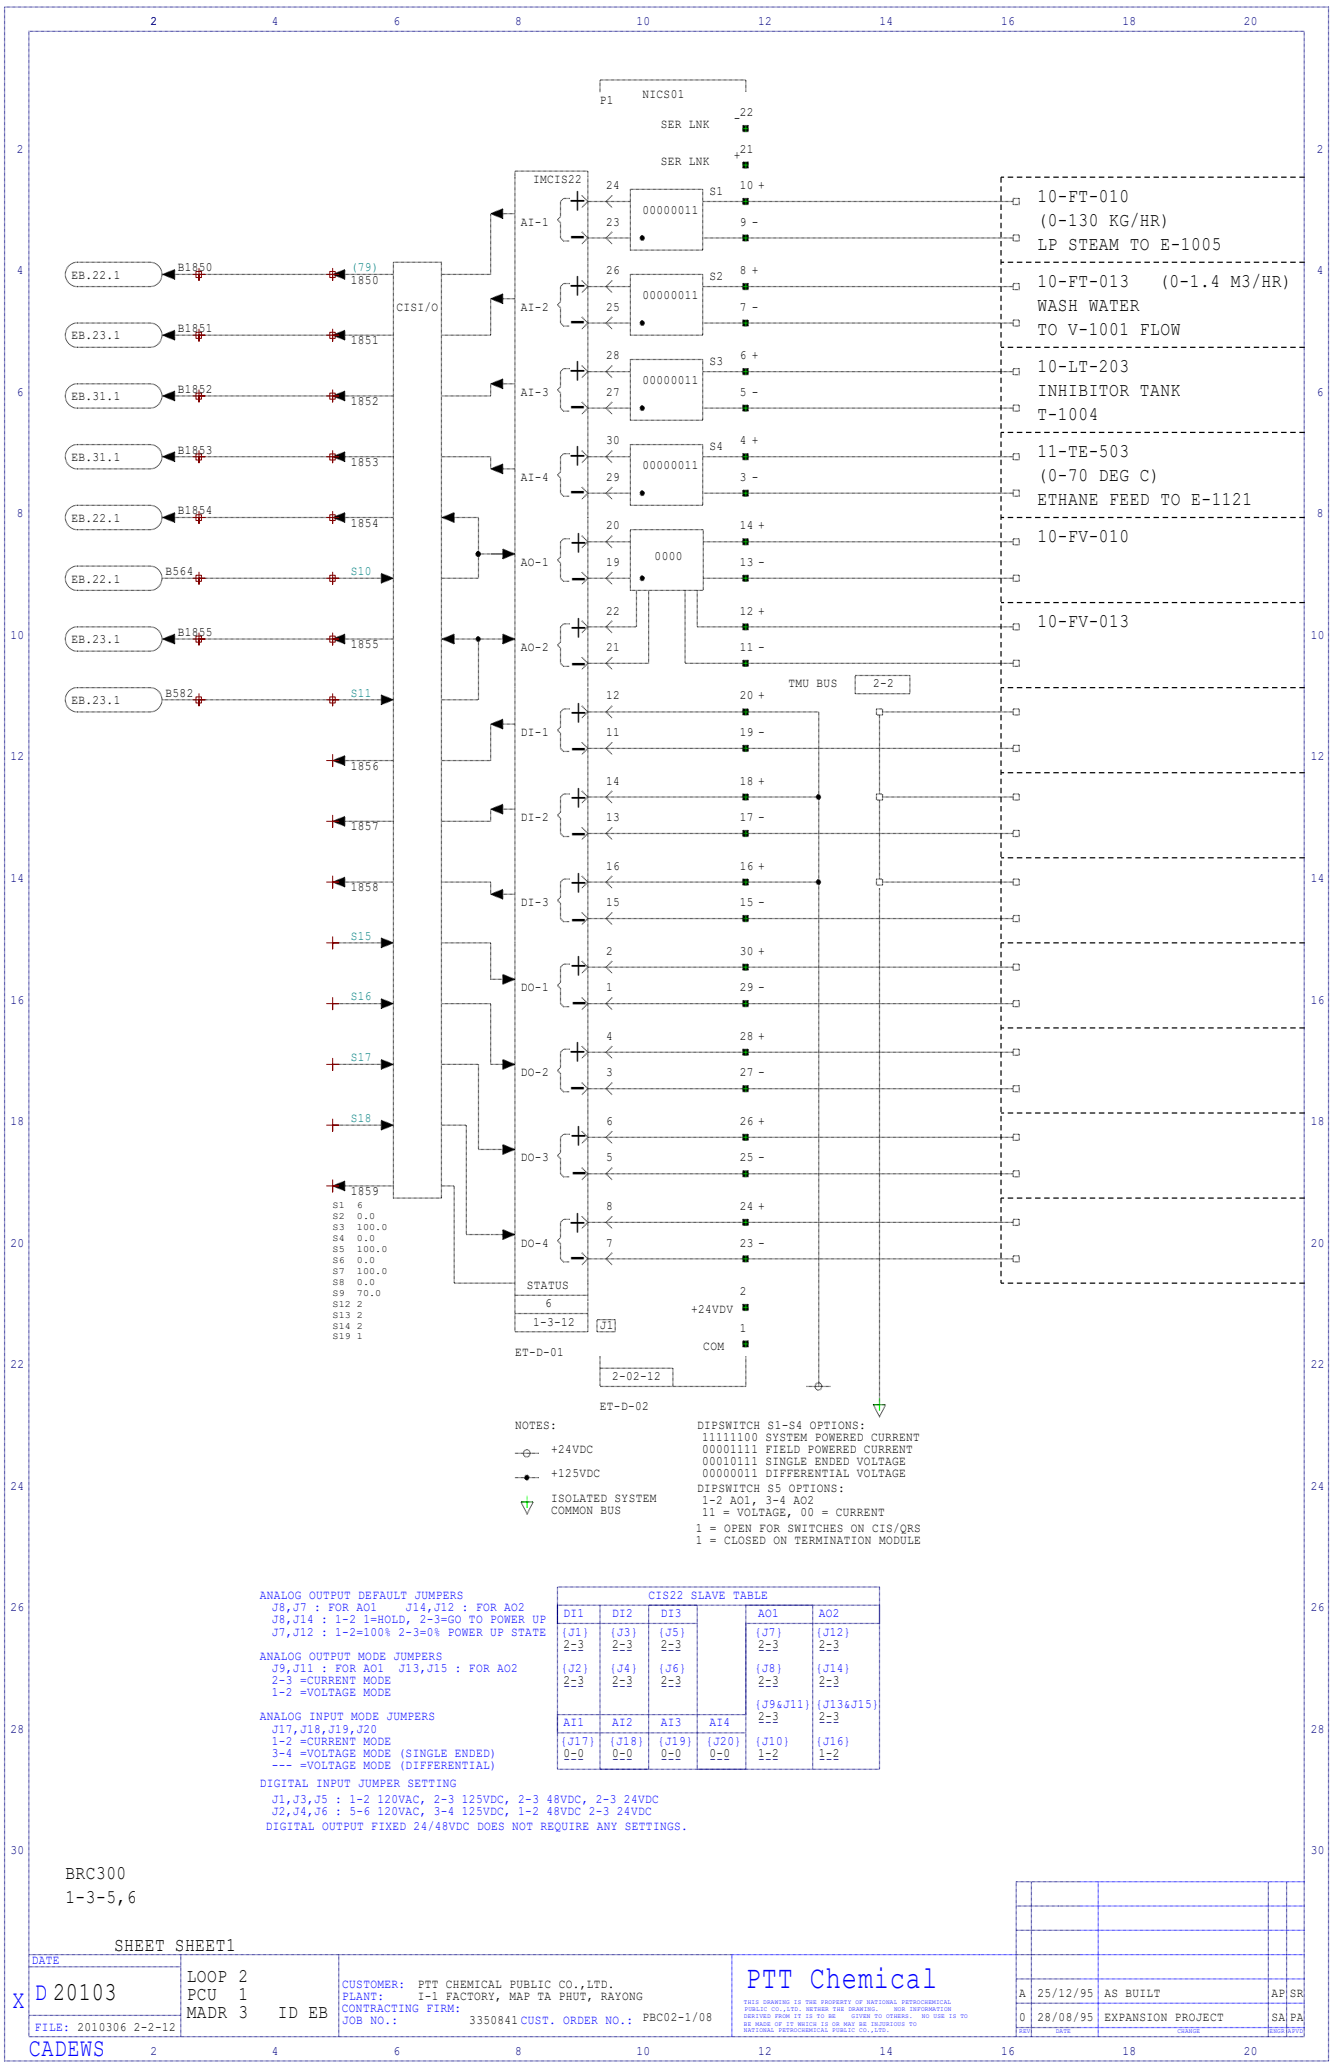

P1
NICS01
SER LNK -22
SER LNK +21
IMCIS22
CISI/O
AI-1
AI-2
AI-3
AI-4
AO-1
AO-2
DI-1
DI-2
DI-3
DO-1
DO-2
DO-3
DO-4
00000011
0000
EB.22.1
EB.23.1
EB.31.1
B1850
B1851
B1852
B1853
B1854
B564
B1855
B582
1850
1851
1852
1853
1854
1855
1856
1857
1858
1859
S10
S11
S15
S16
S17
S18
S1 6
S2 0.0
S3 100.0
S4 0.0
S5 100.0
S6 0.0
S7 100.0
S8 0.0
S9 70.0
S12 2
S13 2
S14 2
S19 1
STATUS
1-3-12
J1
ET-D-01
2-02-12
ET-D-02
+24VDV
COM
TMU BUS
2-2
10-FT-010
(0-130 KG/HR)
LP STEAM TO E-1005
10-FT-013 (0-1.4 M3/HR)
WASH WATER
TO V-1001 FLOW
10-LT-203
INHIBITOR TANK
T-1004
11-TE-503
(0-70 DEG C)
ETHANE FEED TO E-1121
10-FV-010
10-FV-013
NOTES:
+24VDC
+125VDC
ISOLATED SYSTEM COMMON BUS
DIPSWITCH S1-S4 OPTIONS:
11111100 SYSTEM POWERED CURRENT
00001111 FIELD POWERED CURRENT
00010111 SINGLE ENDED VOLTAGE
00000011 DIFFERENTIAL VOLTAGE
DIPSWITCH S5 OPTIONS:
1-2 AO1, 3-4 AO2
11 = VOLTAGE, 00 = CURRENT
1 = OPEN FOR SWITCHES ON CIS/QRS
1 = CLOSED ON TERMINATION MODULE
ANALOG OUTPUT DEFAULT JUMPERS
J8,J7 : FOR AO1 J14,J12 : FOR AO2
J8,J14 : 1-2 1=HOLD, 2-3=GO TO POWER UP
J7,J12 : 1-2=100% 2-3=0% POWER UP STATE
ANALOG OUTPUT MODE JUMPERS
J9,J11 : FOR AO1 J13,J15 : FOR AO2
2-3 =CURRENT MODE
1-2 =VOLTAGE MODE
ANALOG INPUT MODE JUMPERS
J17,J18,J19,J20
1-2 =CURRENT MODE
3-4 =VOLTAGE MODE (SINGLE ENDED)
--- =VOLTAGE MODE (DIFFERENTIAL)
DIGITAL INPUT JUMPER SETTING
J1,J3,J5 : 1-2 120VAC, 2-3 125VDC, 2-3 48VDC, 2-3 24VDC
J2,J4,J6 : 5-6 120VAC, 3-4 125VDC, 1-2 48VDC 2-3 24VDC
DIGITAL OUTPUT FIXED 24/48VDC DOES NOT REQUIRE ANY SETTINGS.
CIS22 SLAVE TABLE
DI1 DI2 DI3 AO1 AO2
(J1) 2-3 (J3) 2-3 (J5) 2-3 (J7) 2-3 (J12) 2-3
(J2) 2-3 (J4) 2-3 (J6) 2-3 (J8) 2-3 (J14) 2-3
(J9&J11) 2-3 (J13&J15) 2-3
AI1 AI2 AI3 AI4
(J17) 0-0 (J18) 0-0 (J19) 0-0 (J20) 0-0 (J10) 1-2 (J16) 1-2
BRC300
1-3-5,6
SHEET SHEET1
DATE
D 20103
FILE: 2010306 2-2-12
LOOP 2
PCU 1
MADR 3 ID EB
CUSTOMER: PTT CHEMICAL PUBLIC CO.,LTD.
PLANT: I-1 FACTORY, MAP TA PHUT, RAYONG
CONTRACTING FIRM:
JOB NO.: 3350841 CUST. ORDER NO.: PBC02-1/08
PTT Chemical
THIS DRAWING IS THE PROPERTY OF NATIONAL PETROCHEMICAL PUBLIC CO.,LTD. NEITHER THE DRAWING, NOR INFORMATION DERIVED FROM IT IS TO BE GIVEN TO OTHERS. NO USE IS TO BE MADE OF IT WHICH IS OR MAY BE INJURIOUS TO NATIONAL PETROCHEMICAL PUBLIC CO.,LTD.
A 25/12/95 AS BUILT AP SR
0 28/08/95 EXPANSION PROJECT SA PA
REV DATE CHANGE ENGR APVD
CADEWS