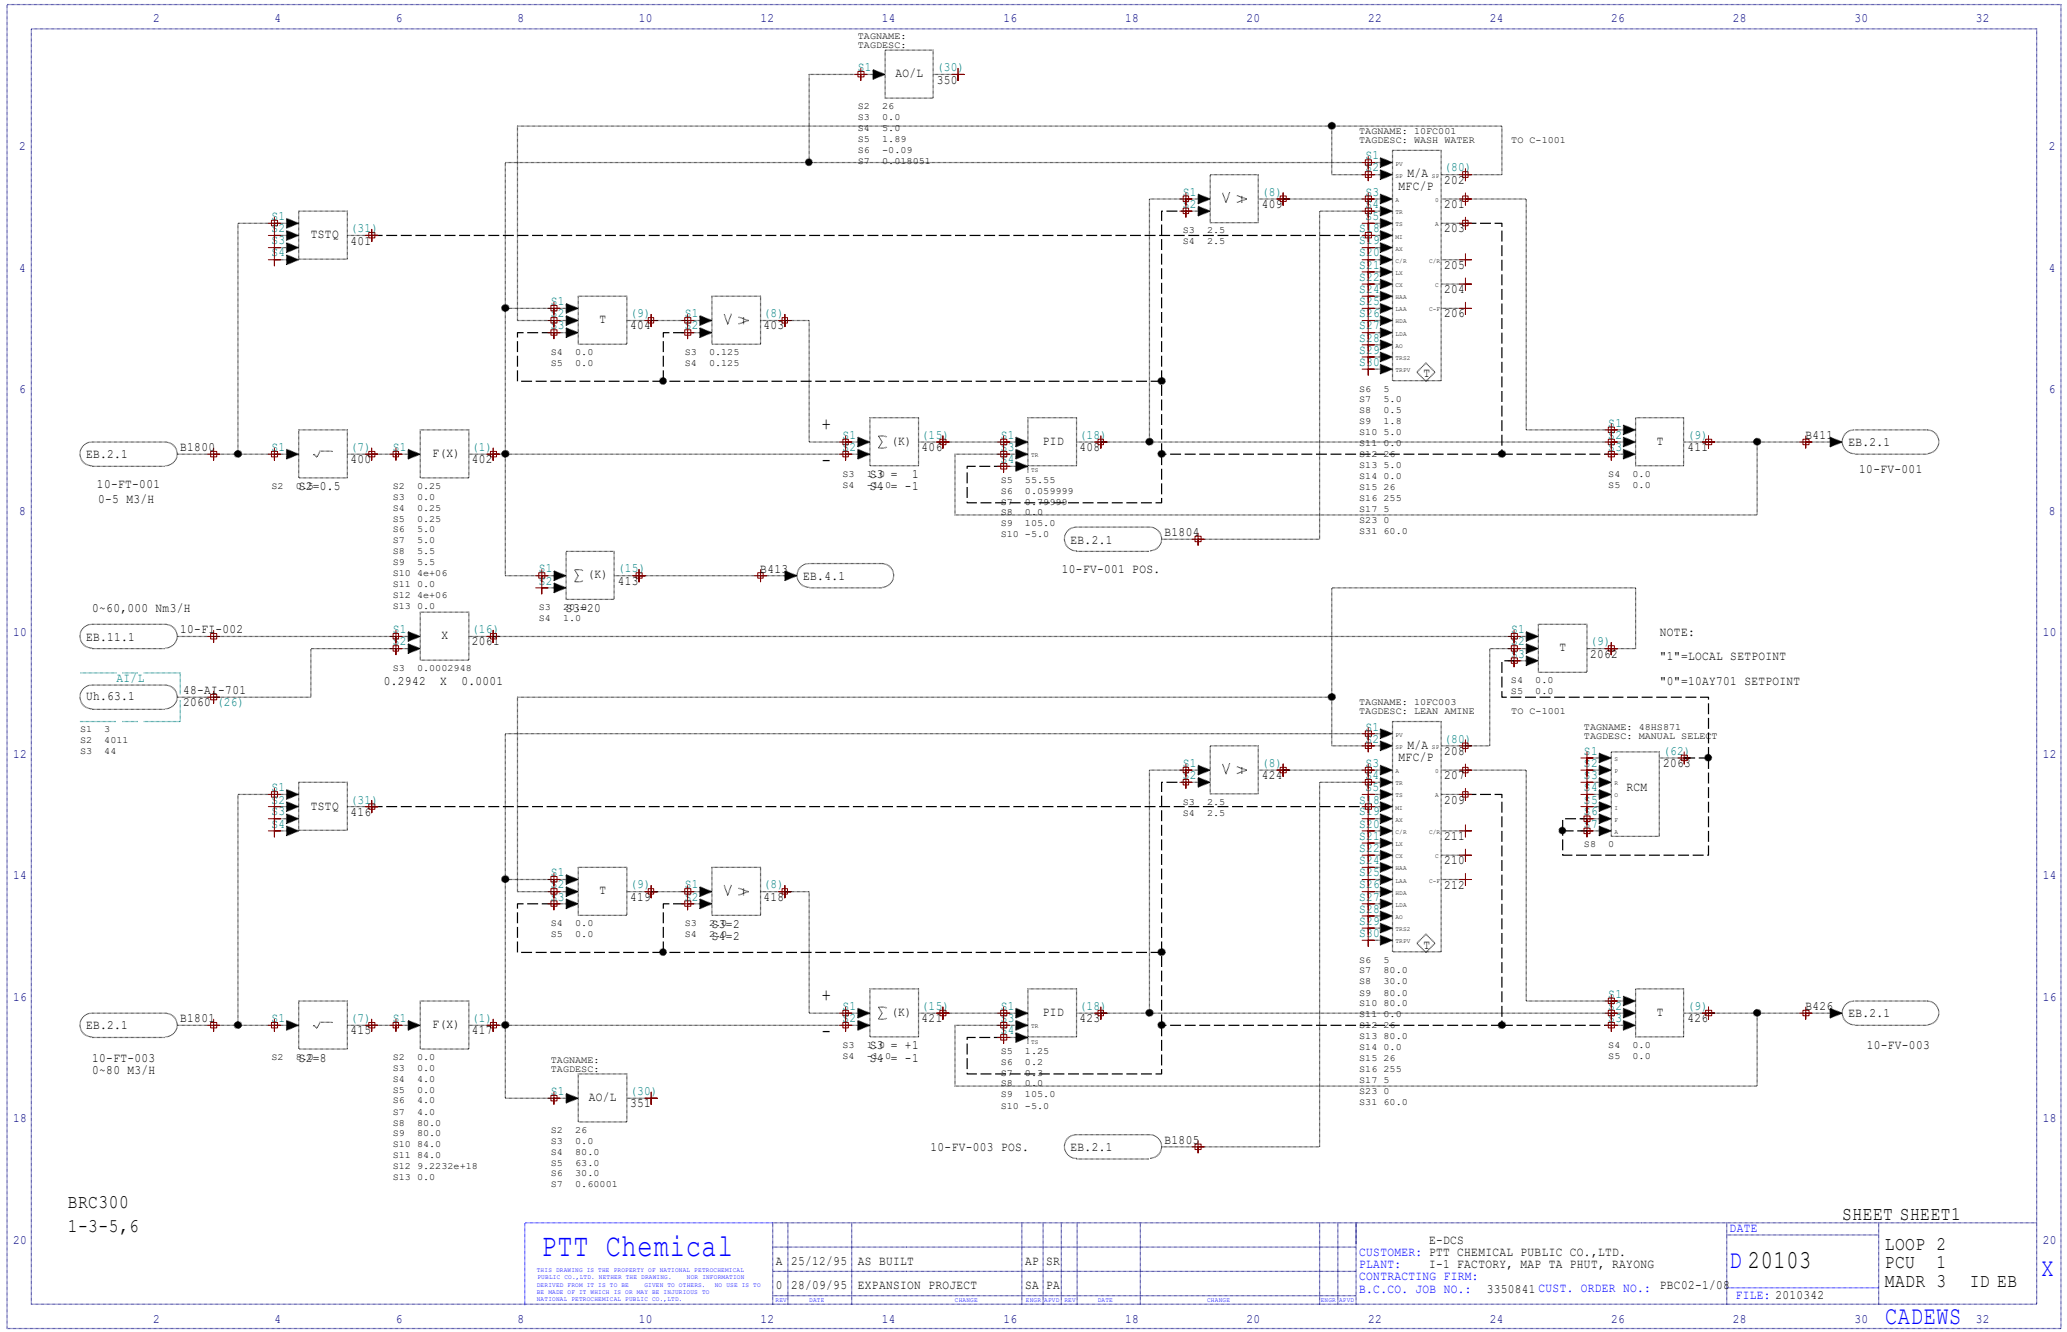

TAGNAME:
TAGDESC:
AO/L
TSTQ
T
PID
F(X)
X
RCM
M/A MFC/P
TAGNAME: 10FC001
TAGDESC: WASH WATER
TO C-1001
TAGNAME: 10FC003
TAGDESC: LEAN AMINE
TAGNAME: 48HS871
TAGDESC: MANUAL SELECT
EB.2.1
B1800
10-FT-001
0-5 M3/H
10-FV-001
B1804
10-FV-001 POS.
B411
B413
EB.4.1
EB.11.1
10-FT-002
0~60,000 Nm3/H
0.2942 X 0.0001
48-AY-701
B1801
10-FT-003
0~80 M3/H
10-FV-003
B1805
10-FV-003 POS.
B426
NOTE:
"1"=LOCAL SETPOINT
"0"=10AY701 SETPOINT
BRC300
1-3-5,6
SHEET SHEET1
PTT Chemical
THIS DRAWING IS THE PROPERTY OF NATIONAL PETROCHEMICAL PUBLIC CO.,LTD. NETHER THE DRAWING NOR INFORMATION DERIVED FROM IT IS TO BE GIVEN TO OTHERS. NO USE IS TO BE MADE OF IT WHICH IS OR MAY BE INJURIOUS TO NATIONAL PETROCHEMICAL PUBLIC CO.,LTD.
A 25/12/95 AS BUILT AP SR
0 28/09/95 EXPANSION PROJECT SA PA
E-DCS
CUSTOMER: PTT CHEMICAL PUBLIC CO.,LTD.
PLANT: I-1 FACTORY, MAP TA PHUT, RAYONG
CONTRACTING FIRM:
B.C.CO. JOB NO.: 3350841 CUST. ORDER NO.: PBC02-1/03
DATE
D 20103
FILE: 2010342
LOOP 2
PCU 1
MADR 3 ID EB
CADEWS