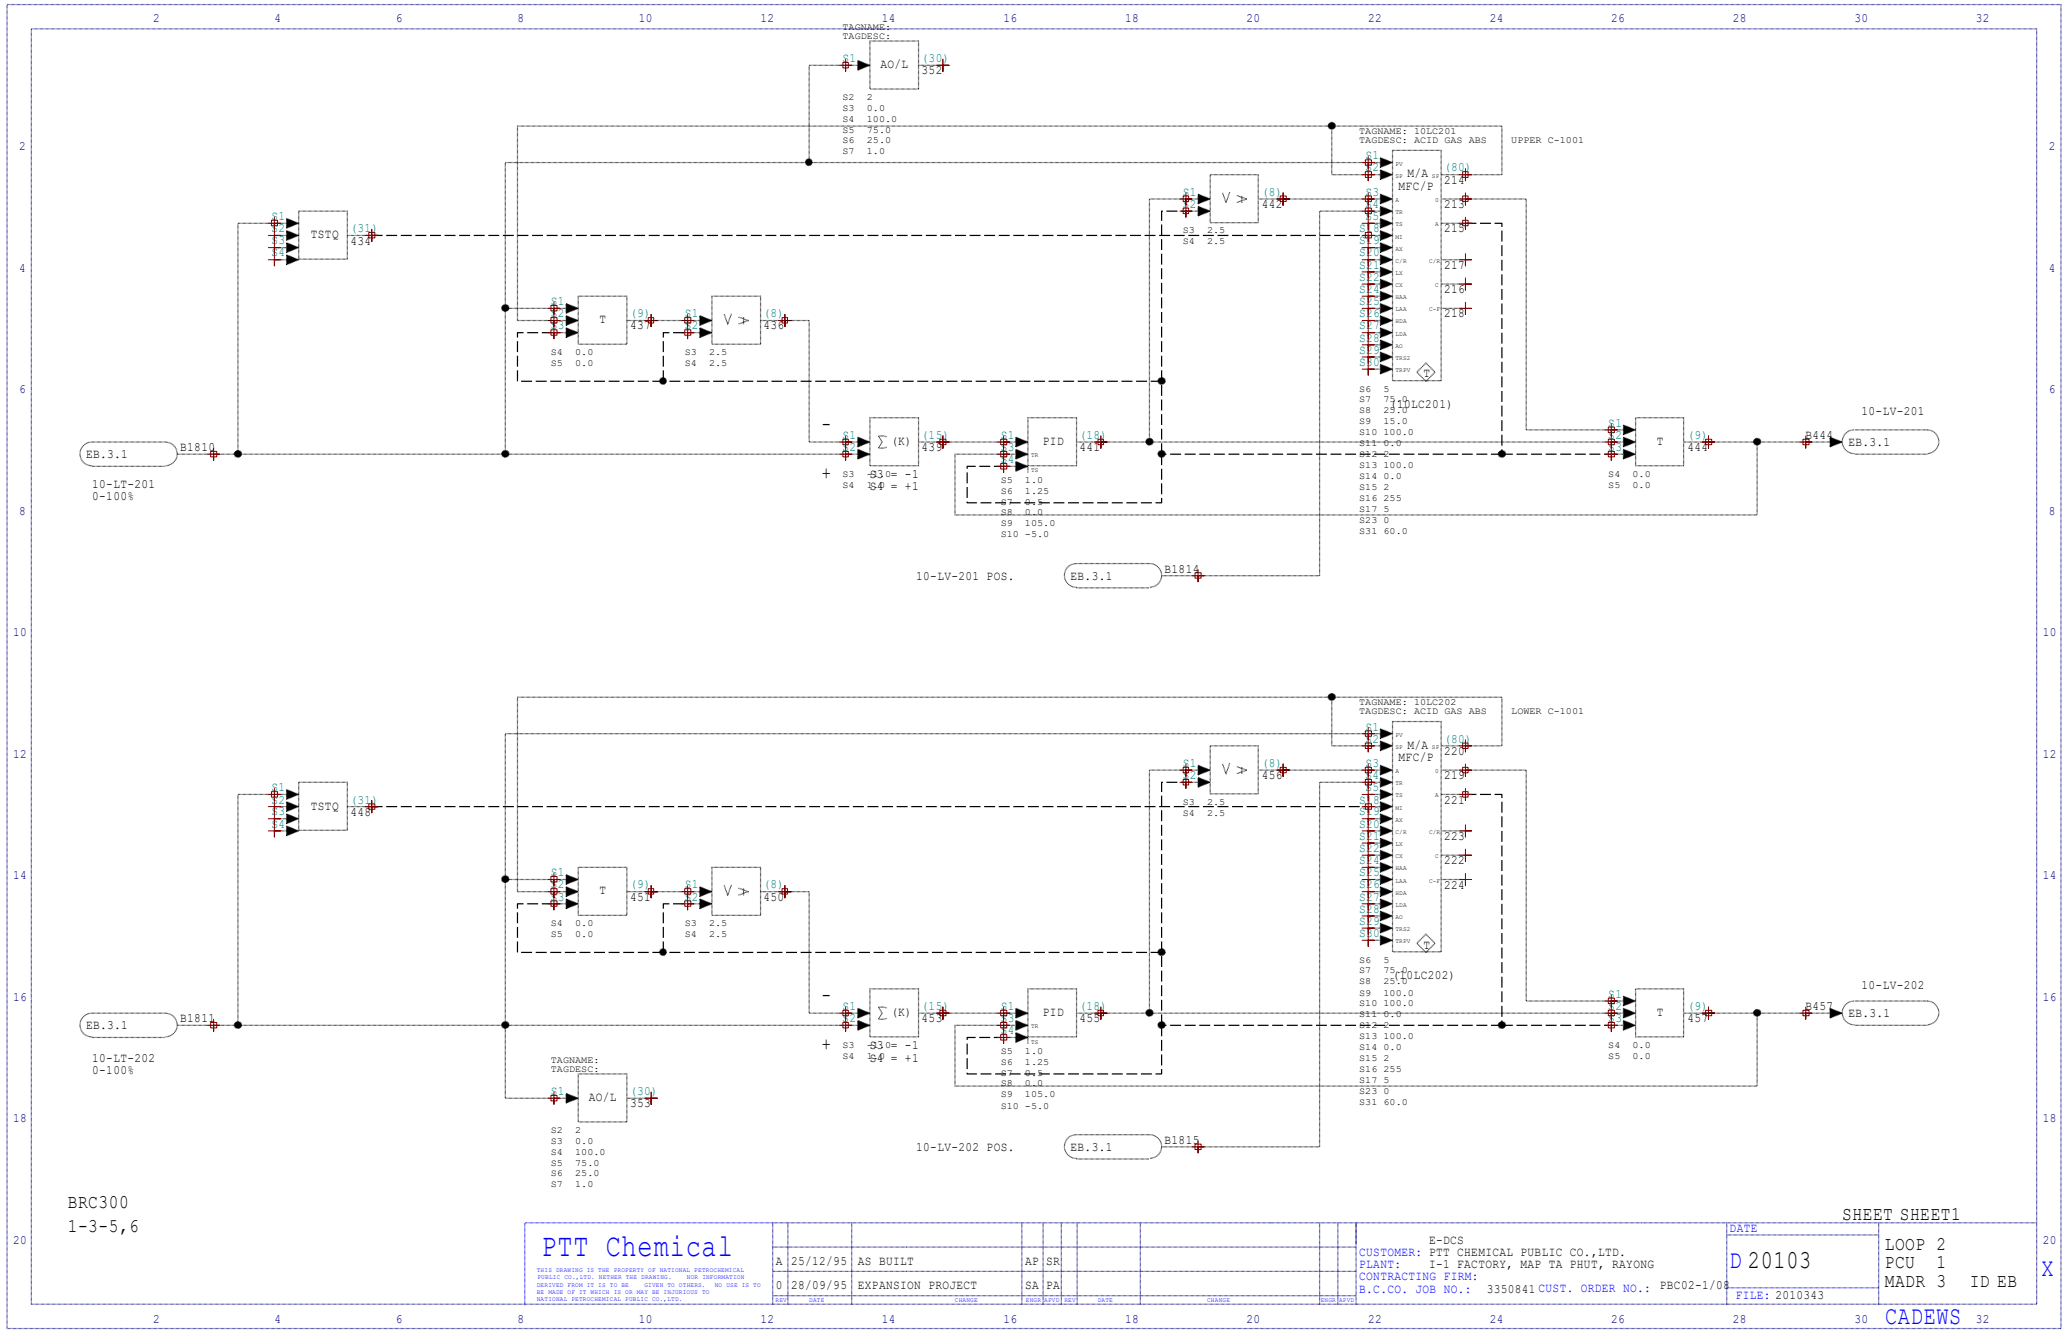

TAGNAME:
TAGDESC:
AO/L
352
TSTQ
434
T
437
V >
438
V >
442
TAGNAME: 10LC201
TAGDESC: ACID GAS ABS
UPPER C-1001
M/A
MFC/P
214
215
217
216
218
(10LC201)
∑ (K)
439
PID
441
T
444
EB.3.1
B1810
10-LT-201
0-100%
10-LV-201
B444
10-LV-201 POS.
B1814
TSTQ
448
T
451
V >
450
V >
456
TAGNAME: 10LC202
TAGDESC: ACID GAS ABS
LOWER C-1001
M/A
MFC/P
220
221
223
222
224
(10LC202)
∑ (K)
453
PID
455
T
457
B1811
10-LT-202
0-100%
10-LV-202
B457
10-LV-202 POS.
B1815
TAGNAME:
TAGDESC:
AO/L
353
BRC300
1-3-5,6
SHEET SHEET1
PTT Chemical
THIS DRAWING IS THE PROPERTY OF NATIONAL PETROCHEMICAL PUBLIC CO.,LTD. NETHER THE DRAWING. NOR INFORMATION DERIVED FROM IT IS TO BE GIVEN TO OTHERS. NO USE IS TO BE MADE OF IT WHICH IS OR MAY BE INJURIOUS TO NATIONAL PETROCHEMICAL PUBLIC CO.,LTD.
A 25/12/95 AS BUILT AP SR
0 28/09/95 EXPANSION PROJECT SA PA
E-DCS
CUSTOMER: PTT CHEMICAL PUBLIC CO.,LTD.
PLANT: I-1 FACTORY, MAP TA PHUT, RAYONG
CONTRACTING FIRM:
B.C.CO. JOB NO.: 3350841 CUST. ORDER NO.: PBC02-1/08
DATE
D 20103
FILE: 2010343
LOOP 2
PCU 1
MADR 3 ID EB
CADEWS