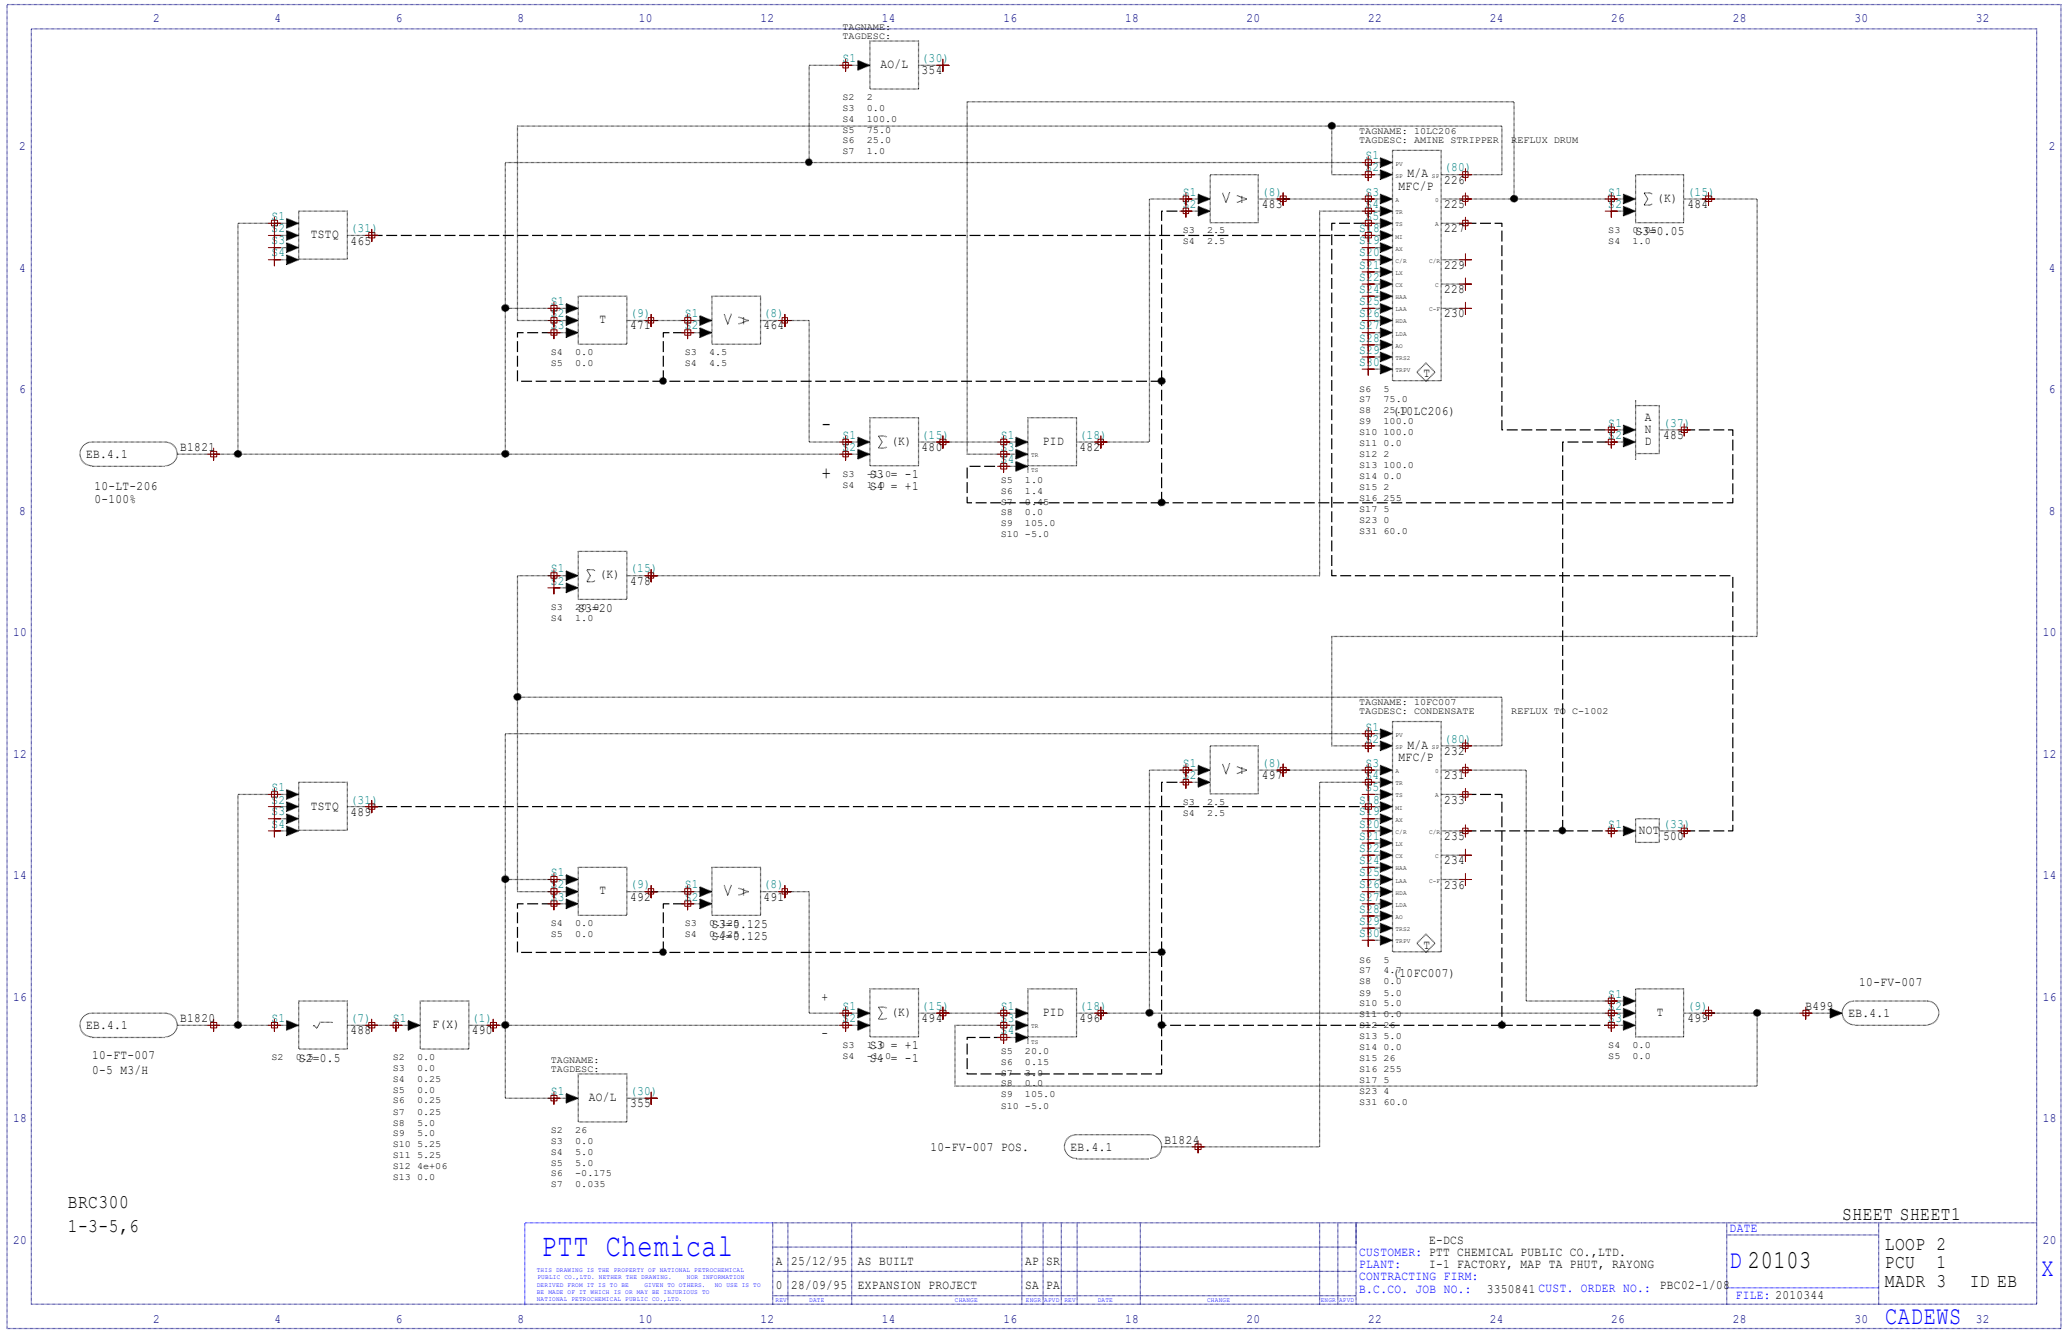

TAGNAME:
TAGDESC:
AO/L
TSTQ
T
PID
F(X)
M/A MFC/P
TAGNAME: 10LC206
TAGDESC: AMINE STRIPPER REFLUX DRUM
TAGNAME: 10FC007
TAGDESC: CONDENSATE REFLUX TO C-1002
EB.4.1
B1821
10-LT-206
0-100%
B1820
10-FT-007
0-5 M3/H
10-FV-007
10-FV-007 POS.
B1824
B499
BRC300
1-3-5,6
PTT Chemical
THIS DRAWING IS THE PROPERTY OF NATIONAL PETROCHEMICAL PUBLIC CO.,LTD. NETHER THE DRAWING. NOR INFORMATION DERIVED FROM IT IS TO BE GIVEN TO OTHERS. NO USE IS TO BE MADE OF IT WHICH IS OR MAY BE INJURIOUS TO NATIONAL PETROCHEMICAL PUBLIC CO.,LTD.
A 25/12/95 AS BUILT AP SR
0 28/09/95 EXPANSION PROJECT SA PA
E-DCS
CUSTOMER: PTT CHEMICAL PUBLIC CO.,LTD.
PLANT: I-1 FACTORY, MAP TA PHUT, RAYONG
CONTRACTING FIRM:
B.C.CO. JOB NO.: 3350841 CUST. ORDER NO.: PBC02-1/08
DATE
D 20103
FILE: 2010344
SHEET SHEET1
LOOP 2
PCU 1
MADR 3 ID EB
CADEWS