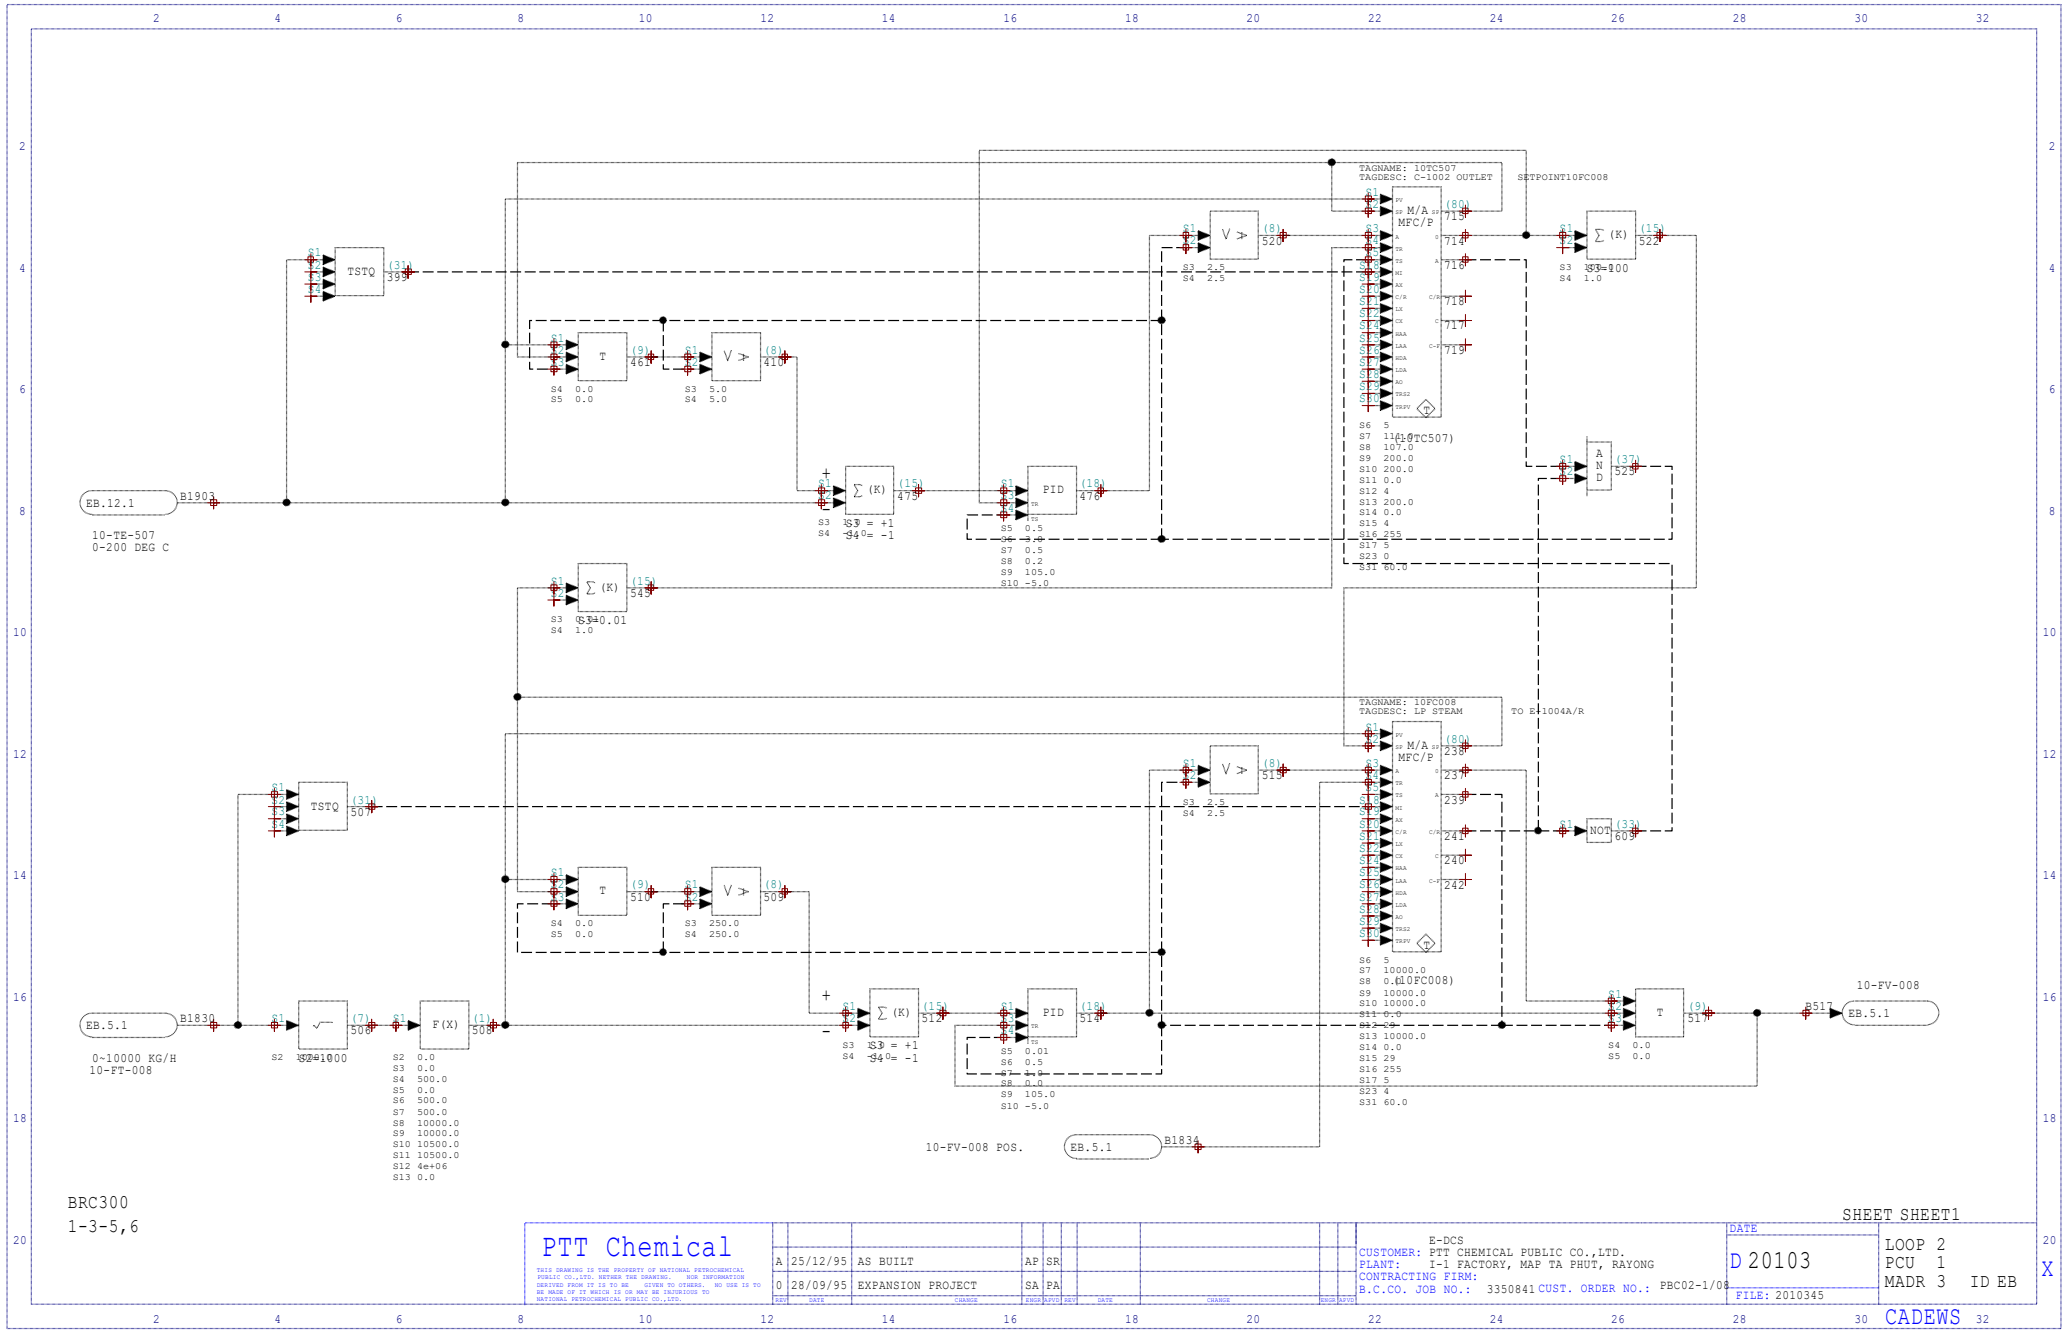

EB.12.1
B1903
10-TE-507
0-200 DEG C
TSTQ
T
PID
M/A MFC/P
TAGNAME: 10TC507
TAGDESC: C-1002 OUTLET
SETPOINT10FC008
AND
NOT
EB.5.1
B1830
0~10000 KG/H
10-FT-008
F(X)
TAGNAME: 10FC008
TAGDESC: LP STEAM
TO E-1004A/R
10-FV-008
B517
10-FV-008 POS.
B1834
BRC300
1-3-5,6
SHEET SHEET1
PTT Chemical
A 25/12/95 AS BUILT
0 28/09/95 EXPANSION PROJECT
E-DCS
CUSTOMER: PTT CHEMICAL PUBLIC CO.,LTD.
PLANT: I-1 FACTORY, MAP TA PHUT, RAYONG
CONTRACTING FIRM:
B.C.CO. JOB NO.: 3350841 CUST. ORDER NO.: PBC02-1/08
DATE
D 20103
FILE: 2010345
LOOP 2
PCU 1
MADR 3 ID EB
CADEWS