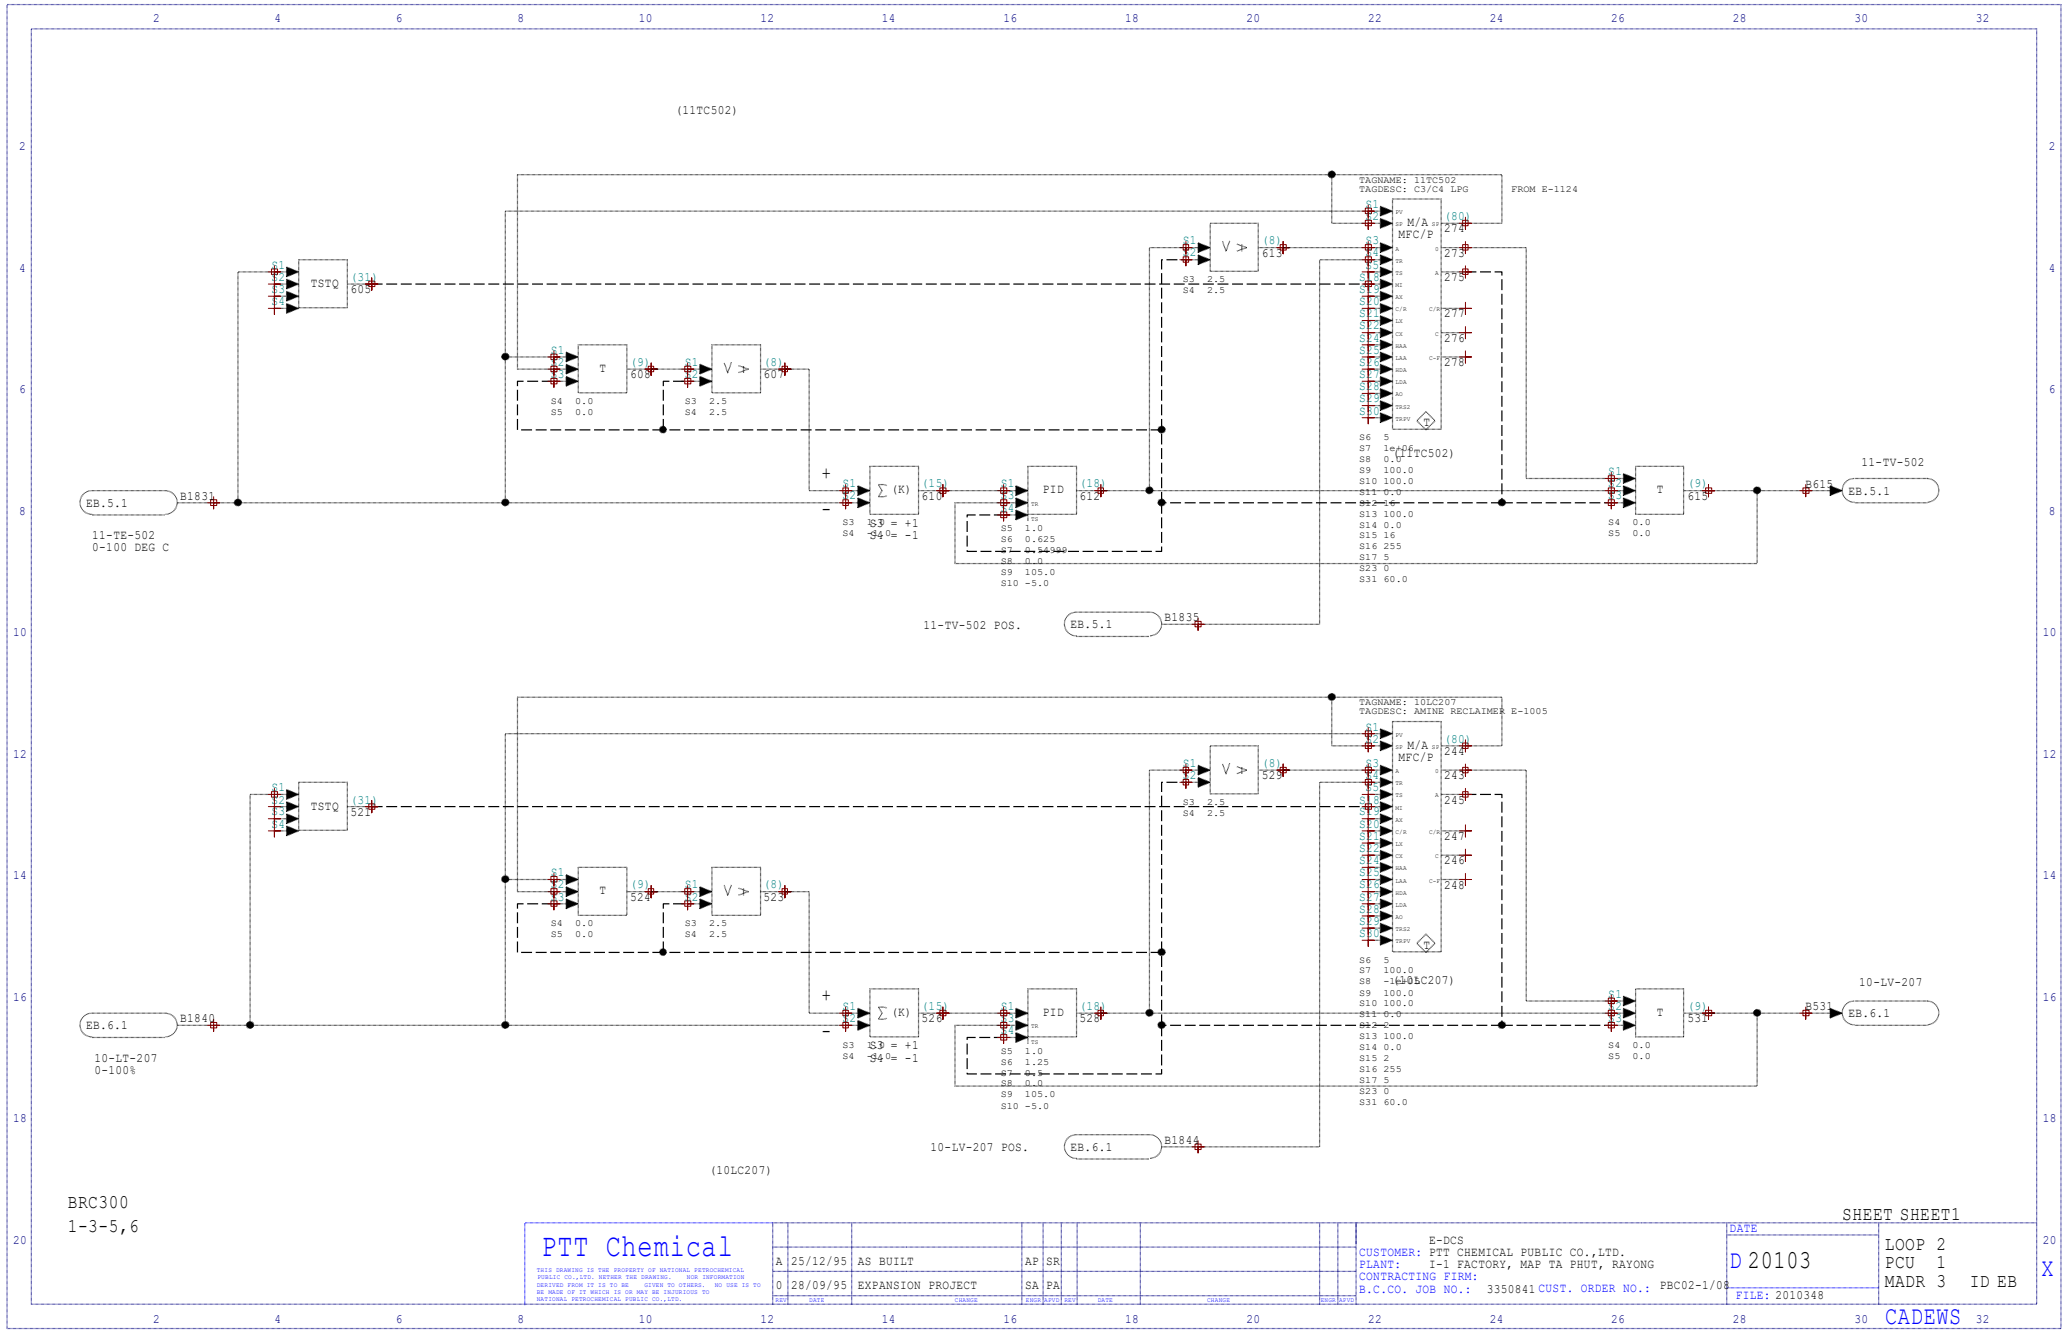

(11TC502)
TAGNAME: 11TC502
TAGDESC: C3/C4 LPG
FROM E-1124
TSTQ
T
V >
∑ (K)
PID
M/A
MFC/P
EB.5.1
B1831
11-TE-502
0-100 DEG C
11-TV-502 POS.
EB.5.1
B1835
11-TV-502
EB.5.1
B615
(10LC207)
TAGNAME: 10LC207
TAGDESC: AMINE RECLAIMER E-1005
EB.6.1
B1840
10-LT-207
0-100%
10-LV-207 POS.
EB.6.1
B1844
10-LV-207
EB.6.1
B531
BRC300
1-3-5,6
SHEET SHEET1
PTT Chemical
THIS DRAWING IS THE PROPERTY OF NATIONAL PETROCHEMICAL PUBLIC CO.,LTD. NEITHER THE DRAWING NOR INFORMATION DERIVED FROM IT IS TO BE GIVEN TO OTHERS. NO USE IS TO BE MADE OF IT WHICH IS OR MAY BE INJURIOUS TO NATIONAL PETROCHEMICAL PUBLIC CO.,LTD.
A 25/12/95 AS BUILT AP SR
0 28/09/95 EXPANSION PROJECT SA PA
E-DCS
CUSTOMER: PTT CHEMICAL PUBLIC CO.,LTD.
PLANT: I-1 FACTORY, MAP TA PHUT, RAYONG
CONTRACTING FIRM:
B.C.CO. JOB NO.: 3350841 CUST. ORDER NO.: PBC02-1/08
DATE
D 20103
FILE: 2010348
LOOP 2
PCU 1
MADR 3 ID EB
CADEWS