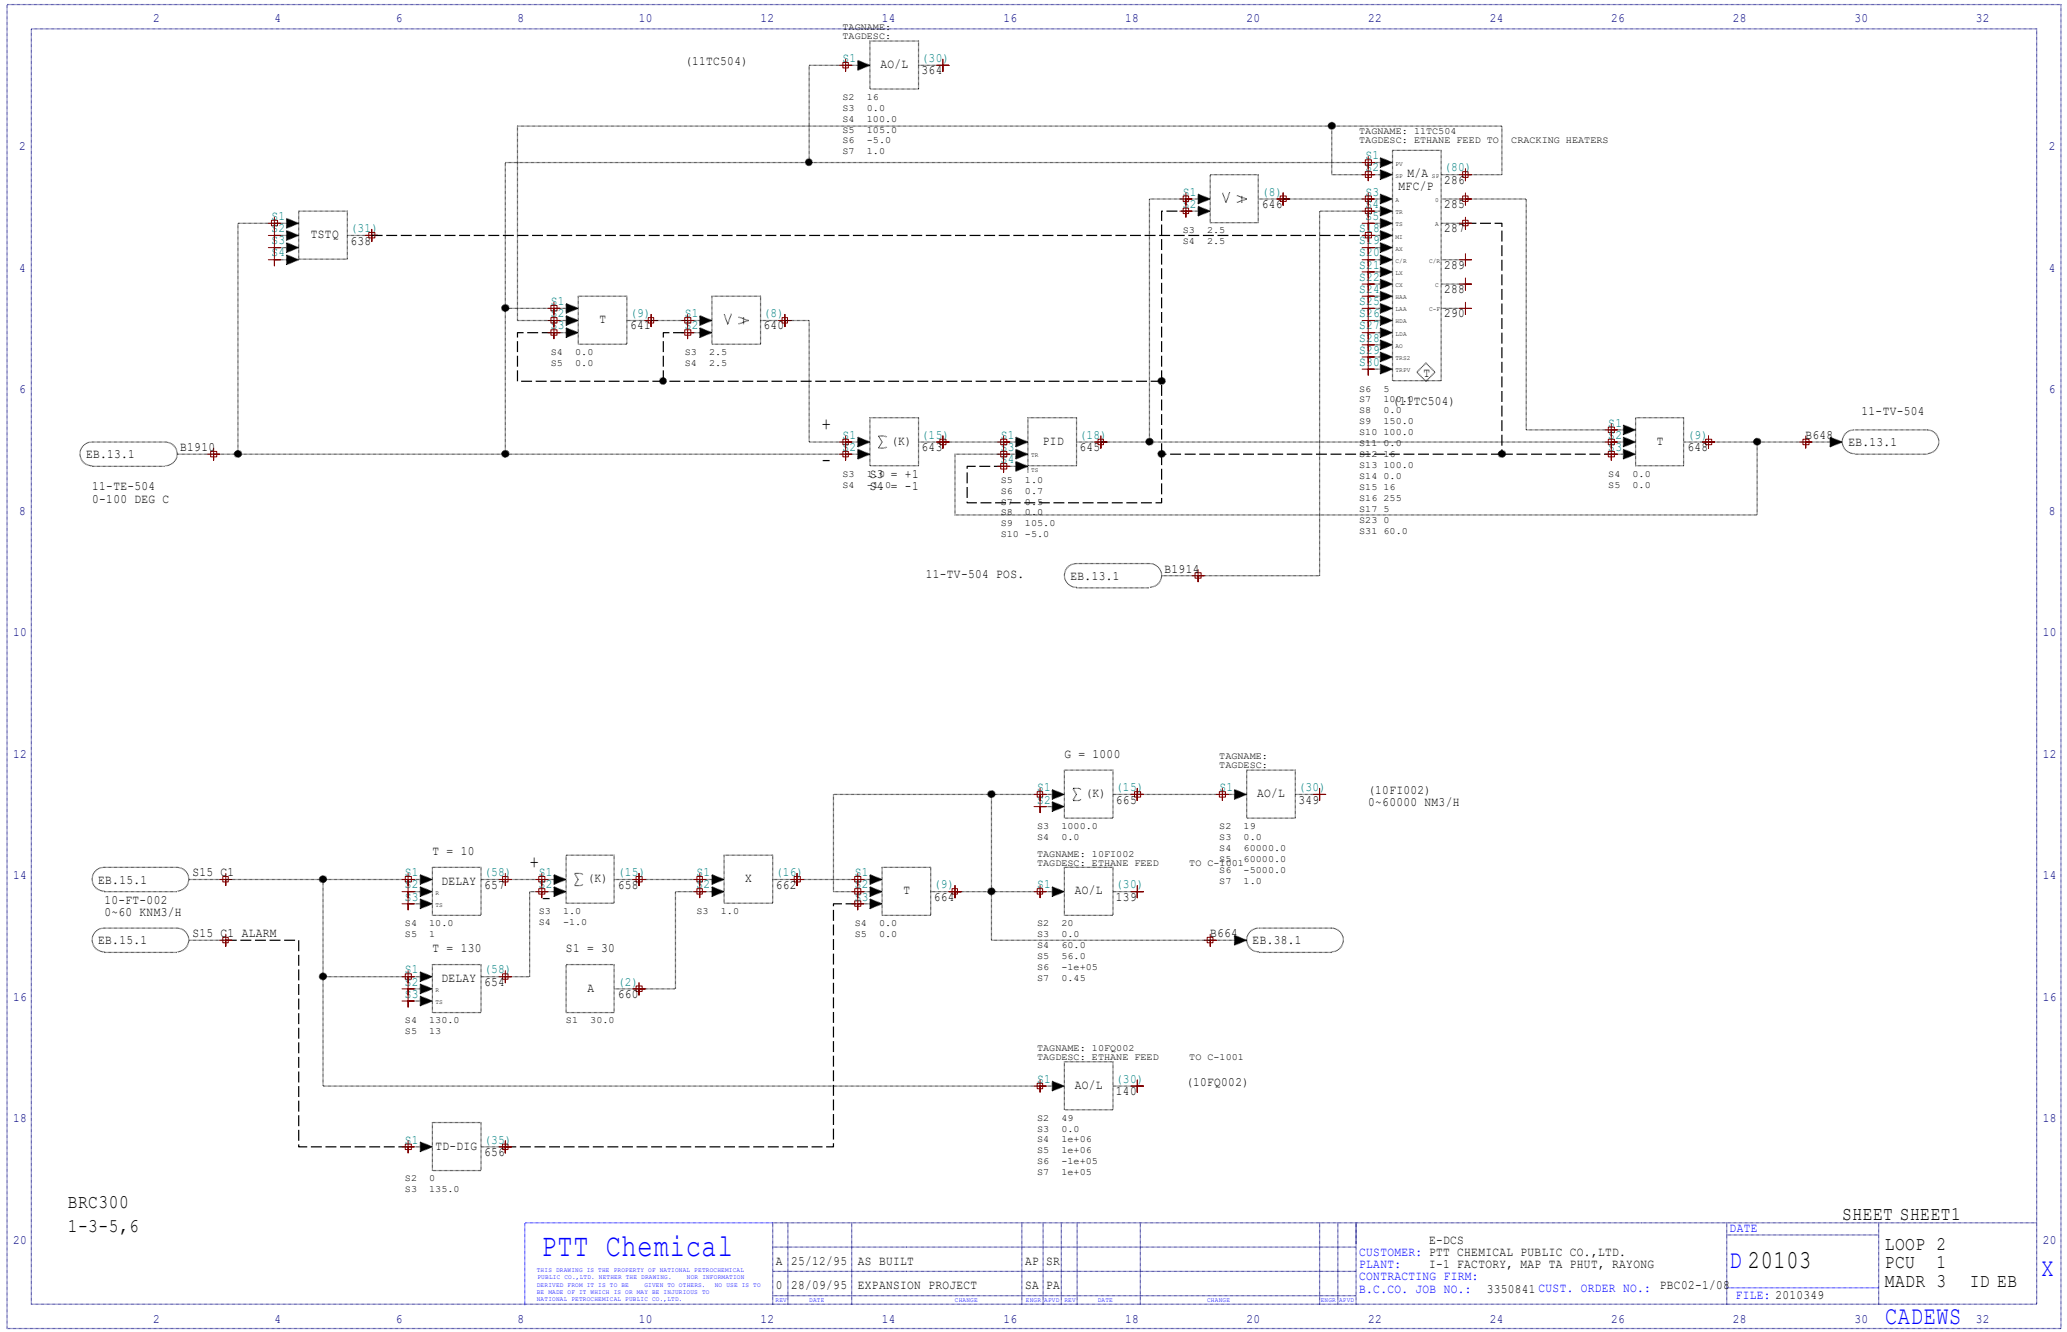

(11TC504)
TAGNAME:
TAGDESC:
AO/L
TSTQ
T
PID
∑ (K)
V >
M/A
MFC/P
TAGNAME: 11TC504
TAGDESC: ETHANE FEED TO CRACKING HEATERS
(11TC504)
EB.13.1
B1910
11-TE-504
0-100 DEG C
11-TV-504
11-TV-504 POS.
B1914
B648
B664
EB.38.1
10-FT-002
0~60 KNM3/H
EB.15.1
S15 C1 ALARM
T = 10
T = 130
DELAY
TD-DIG
A
X
G = 1000
S1 = 30
TAGNAME: 10FI002
TAGDESC: ETHANE FEED
TO C-1001
(10FI002)
0~60000 NM3/H
TAGNAME: 10FQ002
TAGDESC: ETHANE FEED
(10FQ002)
BRC300
1-3-5,6
SHEET SHEET1
PTT Chemical
THIS DRAWING IS THE PROPERTY OF NATIONAL PETROCHEMICAL PUBLIC CO.,LTD. NEITHER THE DRAWING NOR INFORMATION DERIVED FROM IT IS TO BE GIVEN TO OTHERS, NO USE IS TO BE MADE OF IT WHICH IS OR MAY BE INJURIOUS TO NATIONAL PETROCHEMICAL PUBLIC CO.,LTD.
A 25/12/95 AS BUILT AP SR
0 28/09/95 EXPANSION PROJECT SA PA
E-DCS
CUSTOMER: PTT CHEMICAL PUBLIC CO.,LTD.
PLANT: I-1 FACTORY, MAP TA PHUT, RAYONG
CONTRACTING FIRM:
B.C.CO. JOB NO.: 3350841 CUST. ORDER NO.: PBC02-1/08
DATE
D 20103
FILE: 2010349
LOOP 2
PCU 1
MADR 3 ID EB
CADEWS